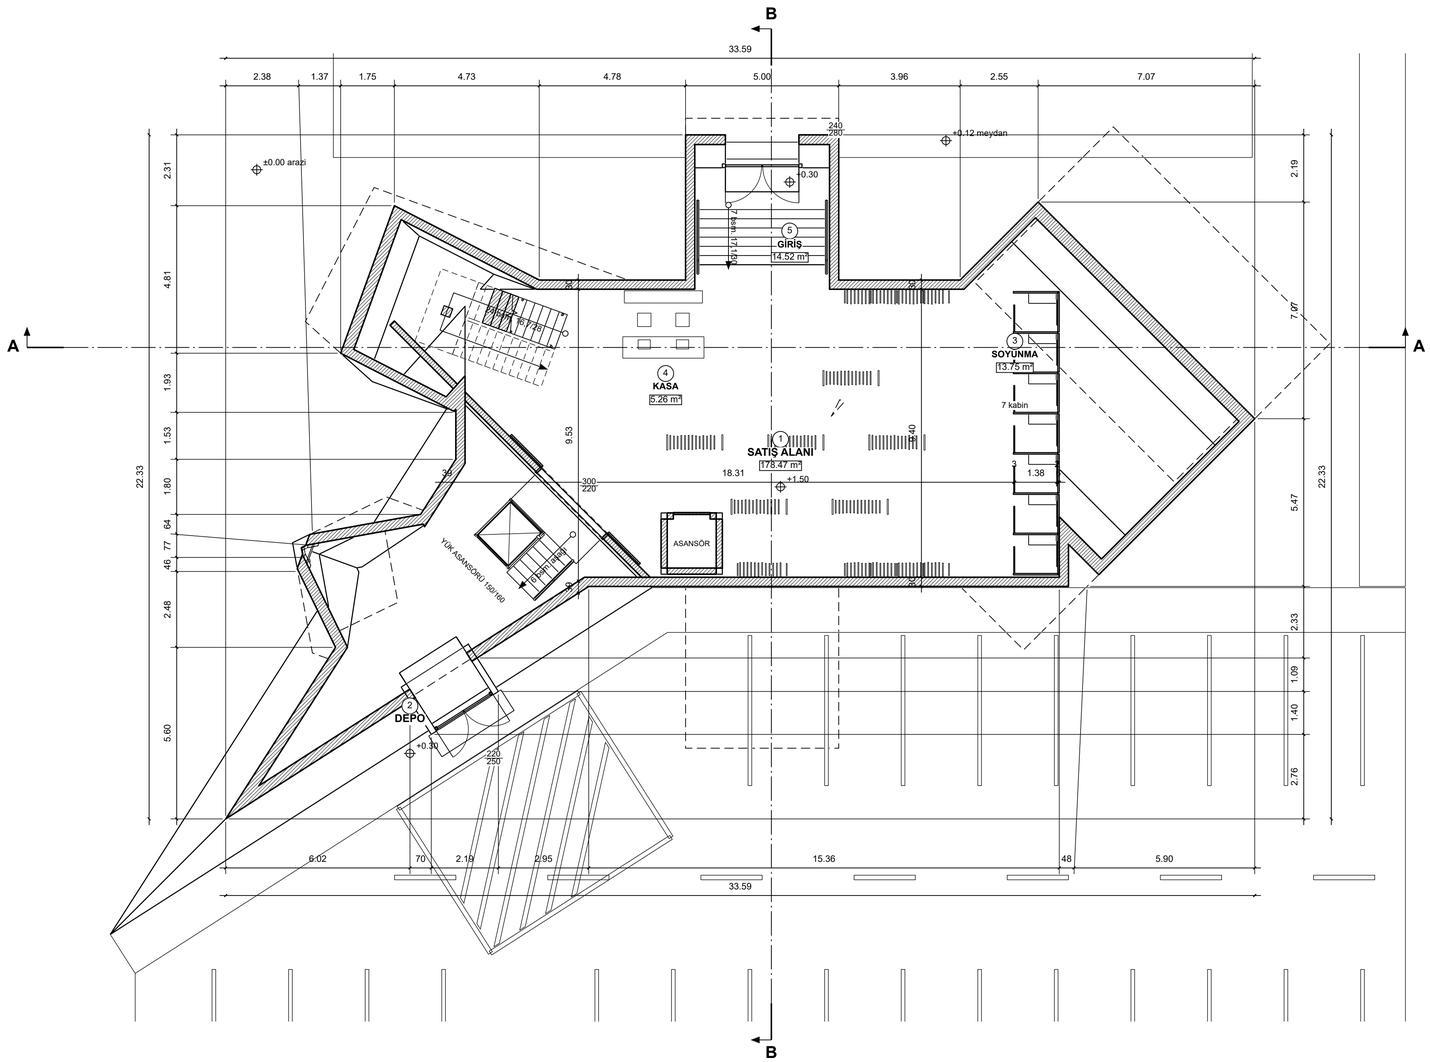


LEJANT

- Betonarme (kesilen)
- Hafif bölme / kabin (kesilen)
- Kesilen eleman sınırı 0,50
- Görünen kenar 0,35
- Tefriş / ölçü 0,25 · 0,18
- Kesit düzlemi üstündeki eleman
- Kesit düzlemi (A–A, B–B)

Ölçüler 1 m altı cm, üstü m.
Kot ±0.00 = arazi (giriş önü).
Pencere/kapı: genişlik üstte, yükseklik altta.
Merdiven: basamak adedi, rıht/basamak (cm).


ZEMİN KAT PLANI

Ölçek 1/100 · Döşeme üstü +1.50 (arazi ±0.00) · Kesit yüksekliği +2.60

0 1 5 10 m

OBLIQUE
MAĞAZA

PROJE	OBLIQUE MAĞAZA – Ticari Yapı
PAFTA	**ZEMİN KAT PLANI**
İÇERİK	Kat planı, iç-dış ölçüler
ÖLÇEK	1/100
PAFTA NO	1 / 5
TARİH	25.10.2026
ÇİZİM	Uygulama öncesi avan proje
BİRİM	Ölçüler m / cm (Neufert)

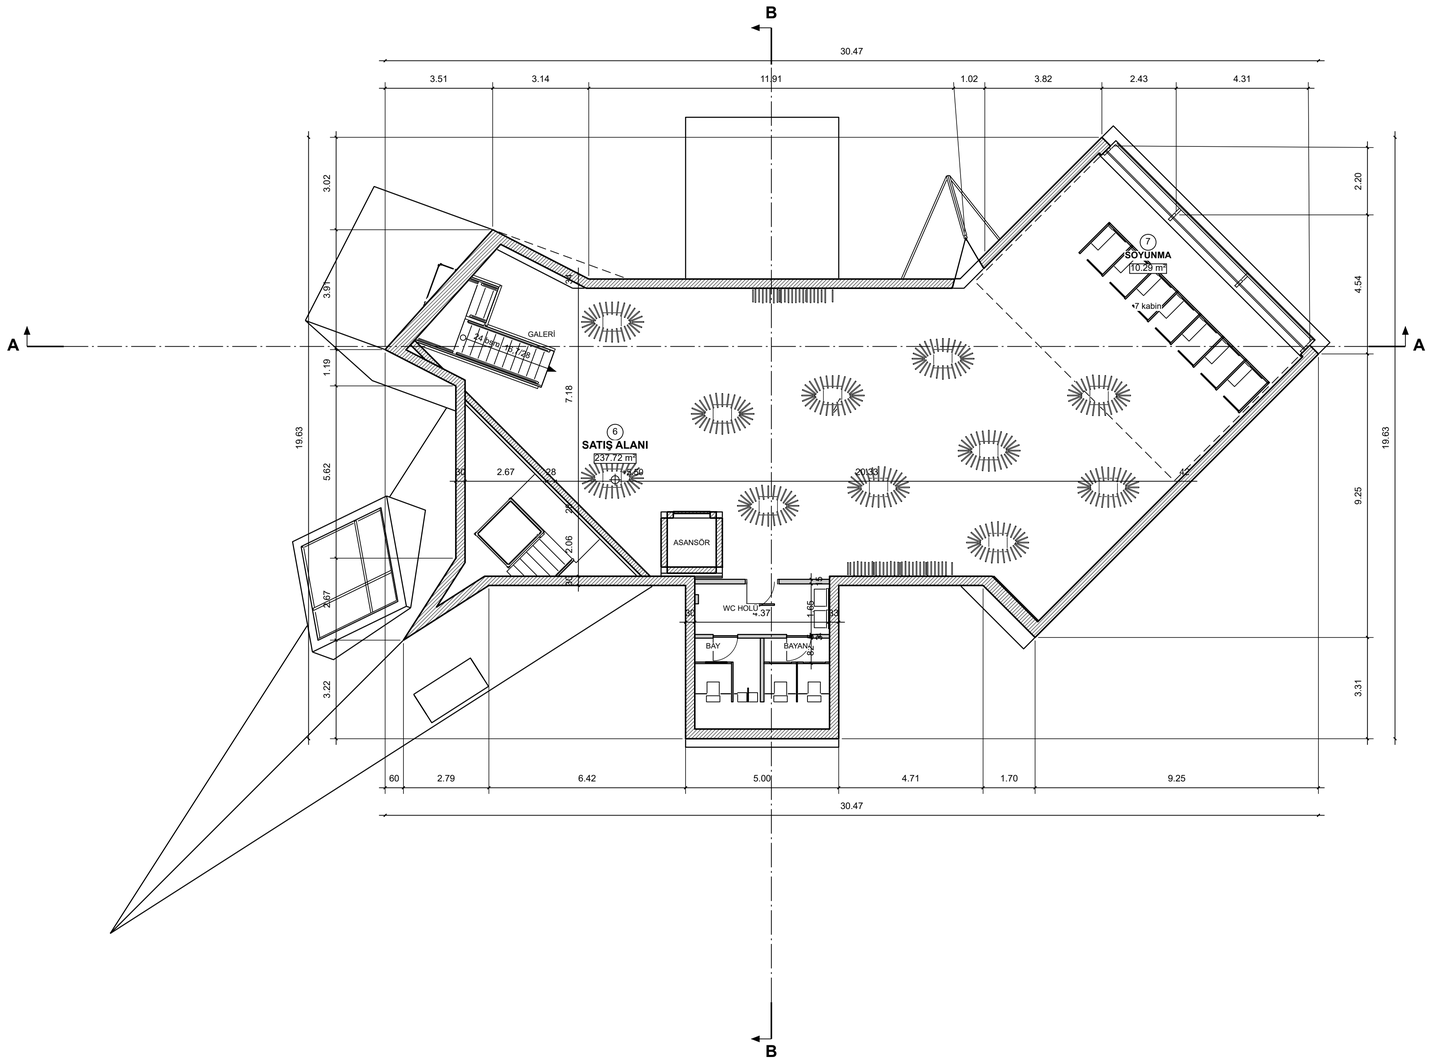

LEJANT

- Betonarme (kesilen)
- Hafif bölme / kabin (kesilen)
- Kesilen eleman sınırı 0,50
- Görünen kenar 0,35
- Tefriş / ölçü 0,25 · 0,18
- Kesit düzlemi üstündeki eleman
- Kesit düzlemi (A–A, B–B)

Ölçüler 1 m altı cm, üstü m.
Kot ±0.00 = arazi (giriş önü).
Pencere/kapı: genişlik üstte, yükseklik altta.
Merdiven: basamak adedi, rıht/basamak (cm).


1. KAT PLANI

Ölçek 1/100 · Döşeme üstü +5.50 · Kesit yüksekliği +6.60


0 1 5 10 m

OBLIQUE MAĞAZA	
PROJE	OBLIQUE MAĞAZA – Ticari Yapı
PAFTA	**1. KAT PLANI**
İÇERİK	Kat planı, iç-dış ölçüler
ÖLÇEK	1/100
PAFTA NO	2 / 5
TARİH	25.10.2026
ÇİZİM	Uygulama öncesi avan proje
BİRİM	Ölçüler m / cm (Neufert)

KESİT A–A

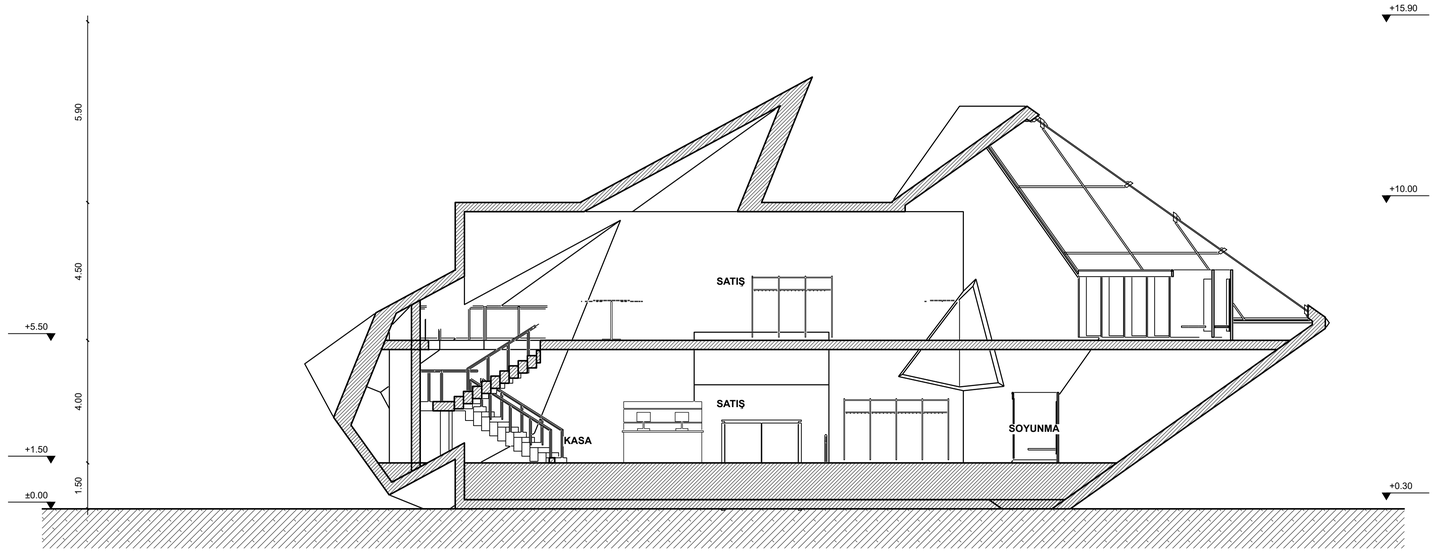

KESİT B–B

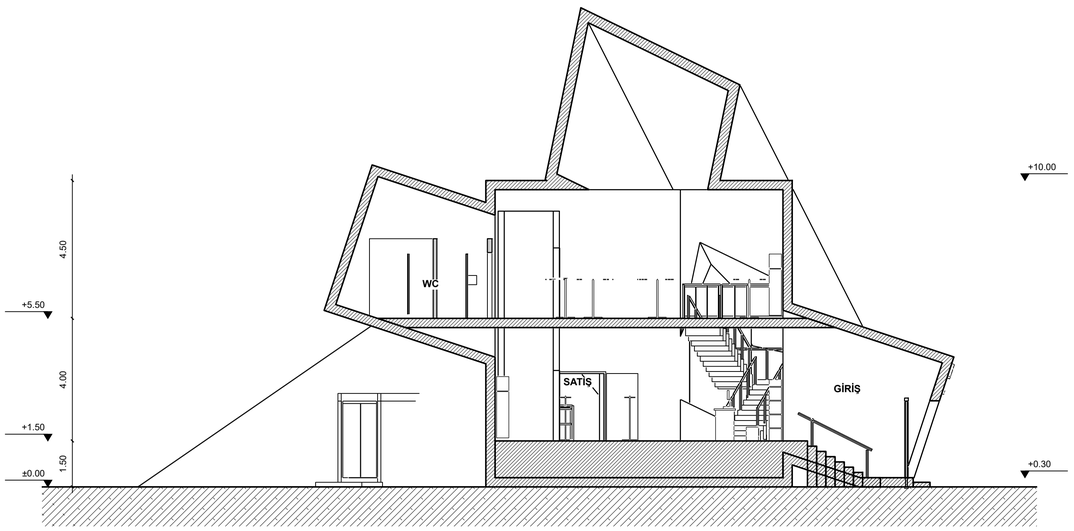




OBLIQUE


MAĞAZA

PROJE	OBLIQUE MAĞAZA – Ticari Yapı
PAFTA	**KESİTLER A–A, B–B**
İÇERİK	Düşey kesitler, kotlar
ÖLÇEK	1/100
PAFTA NO	3 / 5
TARİH	25.10.2026
ÇİZİM	Uygulama öncesi avan proje
BİRİM	Ölçüler m / cm (Neufert)

KUZEY GÖRÜNÜŞÜ (GİRİŞ)

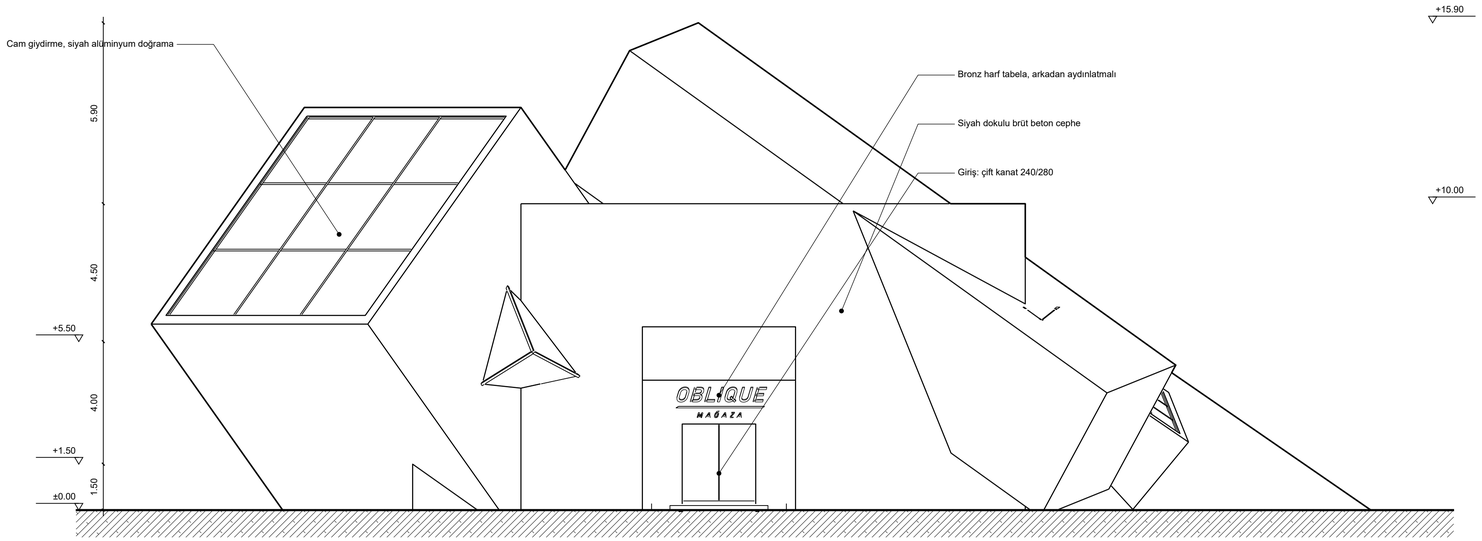

GÜNEY GÖRÜNÜŞÜ (OTOPARK)

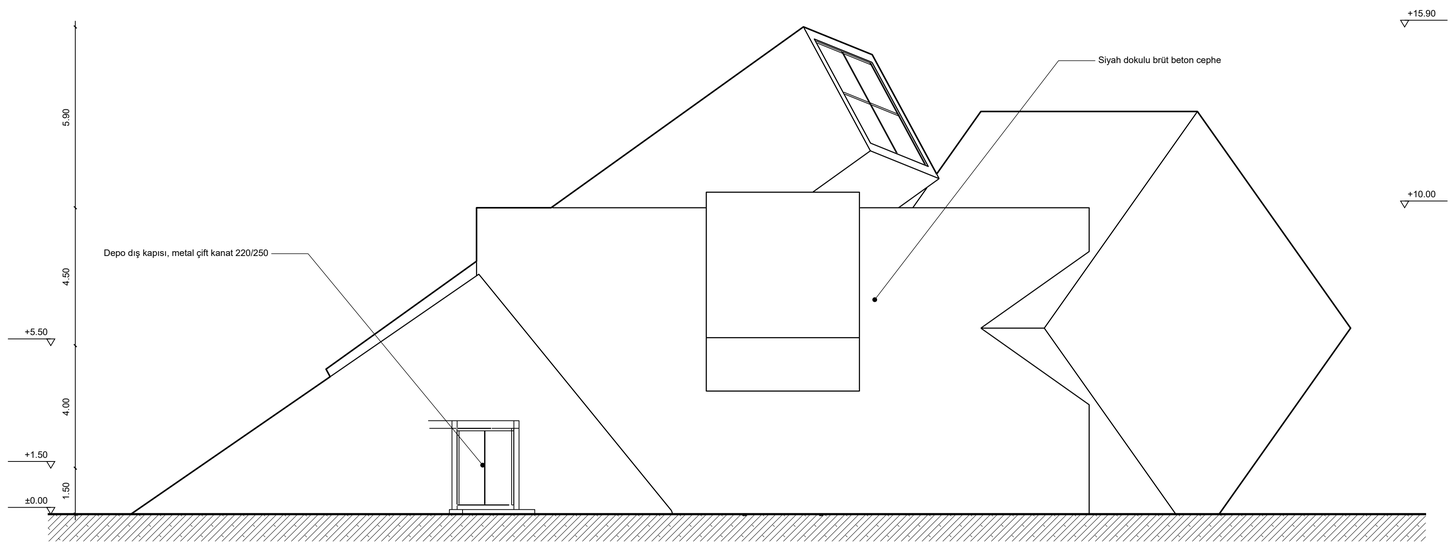


0 1 5 10 m


OBLIQUE
MAĞAZA

PROJE	OBLIQUE MAĞAZA – Ticari Yapı
PAFTA	**GÖRÜNÜŞLER Kuzey – Güney**
İÇERİK	Cepheler, kotlar
ÖLÇEK	1/100
PAFTA NO	4 / 5
TARİH	25.10.2026
ÇİZİM	Uygulama öncesi avan proje
BİRİM	Ölçüler m / cm (Neufert)

DOĞU GÖRÜNÜŞÜ

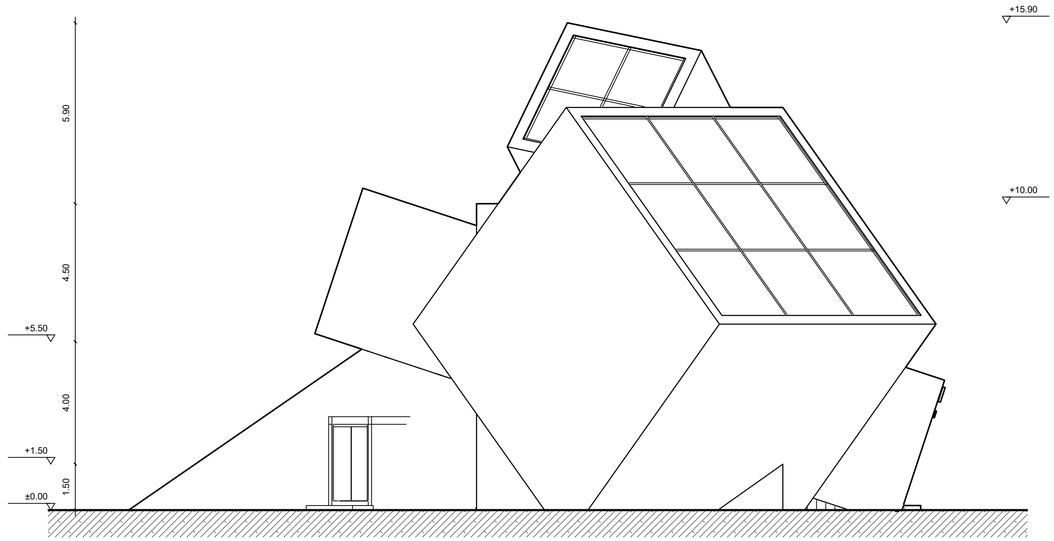

BATI GÖRÜNÜŞÜ

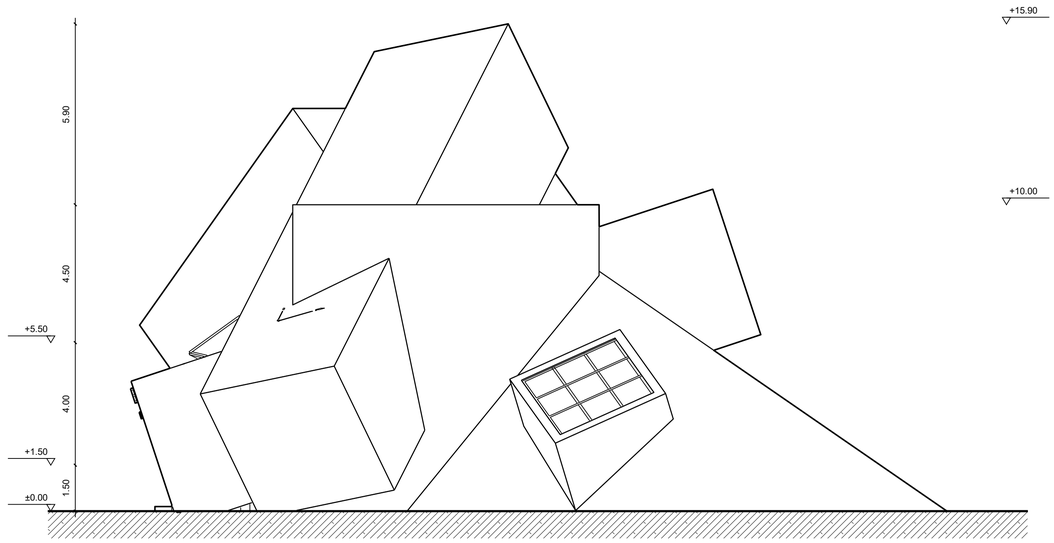

0 1 5 10 m

OBLIQUE

M A Ğ A Z A

PROJE	OBLIQUE MAĞAZA – Ticari Yapı
PAFTA	**GÖRÜNÜŞLER Doğu – Batı**
İÇERİK	Cepheler, kotlar
ÖLÇEK	1/100
PAFTA NO	5 / 5
TARİH	25.10.2026
ÇİZİM	Uygulama öncesi avan proje
BİRİM	Ölçüler m / cm (Neufert)