

VAZİYET PLANI

Ölçek 1/250 · kuzey yukarı

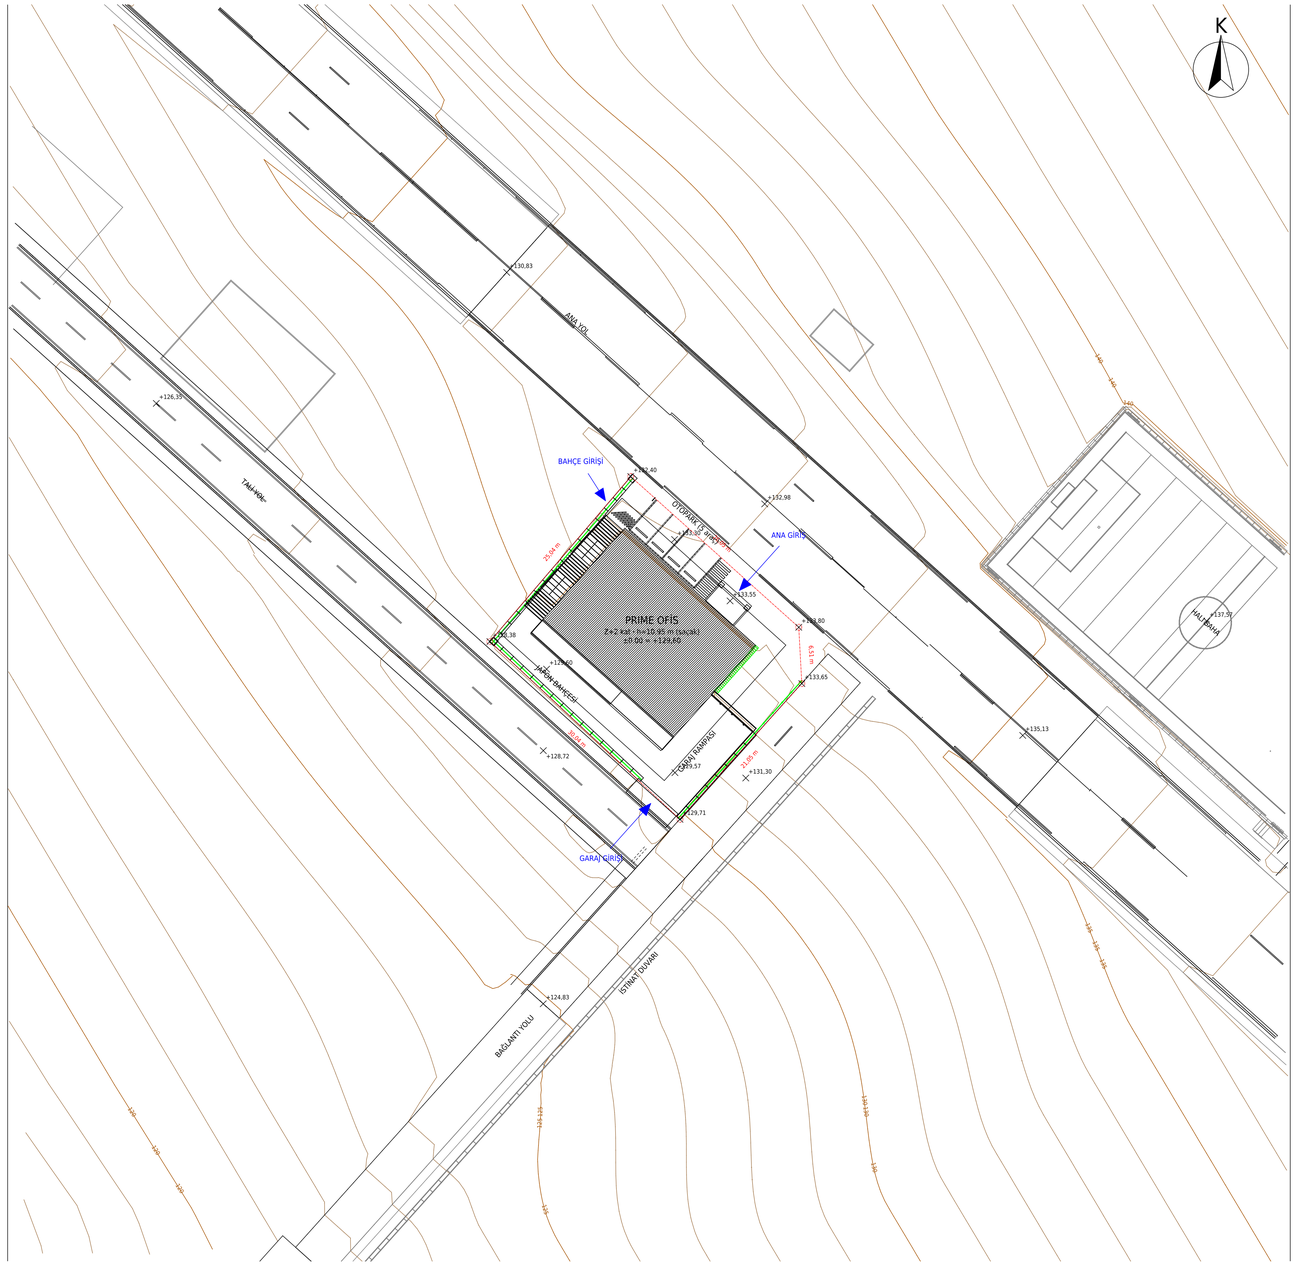

ULAŞIM İLİŞKİLERİ (şematik)

1/5000

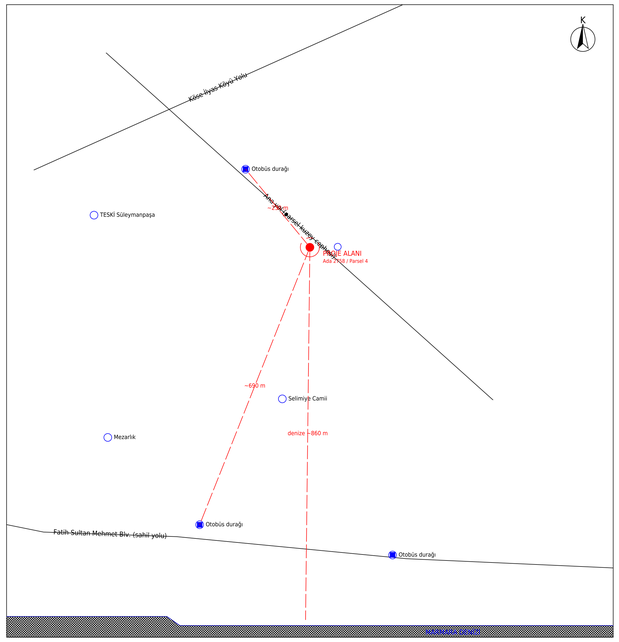

RÜZGÂR GÜLÜ (yıllık frekans)

GÜNEŞ YÖRÜNGESİ (41° K)

İKLİM VERİLERİ – TEKİRDAĞ

	Oca	Şub	Mar	Nis	May	Haz	Tem	Ağu	Eyl	Eki	Kas	Ara
Ort. sıcaklık °C	4,9	5,5	7,4	11,8	16,7	21,2	23,8	23,9	20,3	15,7	11,4	7,3
Ort. en yüksek °C	8,2	9,0	11,1	15,8	20,6	25,4	28,1	28,3	24,6	19,6	14,9	10,5
Ort. en düşük °C	2,1	2,5	4,2	8,1	12,7	16,8	19,1	19,5	16,2	12,1	8,2	4,4
Yağış mm	67,8	54,0	53,0	42,3	37,0	37,4	23,5	15,3	32,4	59,7	73,4	79,3

Yıllık ort. sıcaklık 14,2 °C · Yıllık toplam yağış 575 mm · Yağışlı gün 97,5
En yüksek 40,2 °C (Haziran) · En düşük -13,5 °C (Ocak) · En yüksek kar 44 cm
Hâkim rüzgâr: KB %25,4, KD %20,1, K %17,6 · Ort. rüzgâr hızı 2,7 m/s
En hızlı rüzgâr 41,7 m/s · Ort. bağıl nem %77
Kaynak: MGM Tekirdağ resmî istatistikleri (1940-2025); rüzgâr frekansları: İ.Ü. "Tekirdağ'ın İklim Özellikleri" tezi (1975-2005 rasatları).

NOTLAR

Vaziyet planı kuzey yukarı çizilmiştir; bina eksenleri kuzeyden 41,9° saat yönü tersine döner.

Eş yükselti eğrileri 1 m aralıklı, kalın eğriler 5 m'dir (mutlak kot).

Parsel içinde arazi doğu-kuzeydoğudan batı-güneybatıya doğru yaklaşık %15-17 eğimlidir (parsel köşeleri arası kot farkı 5,4 m); geniş ölçekte arazi güneye, denize doğru iner.

Hesaplanan değerler: bina oturumu 290 m² (TAKS = 0,38), toplam kapalı alan = 870 m² (KAKS = 1,15). İmar durumu belgesi ile kontrol edilecektir.

Yakın çevre bilgileri ve mesafeler harita altlığından ölçülmüş yaklaşık değerlerdir.

LEJANT

- Parsel sınırı (Ada 2758 / P.4)
- Bina oturumu
- Çatı / saçak izdüşümü
- Eş yükselti eğrisi (5 m)
- Eş yükselti eğrisi (1 m)
- Yol / asfalt sınırı
- Kaldırım / bordür
- Giriş / ulaşım

PROJE

PRIME OFİS

3 Katlı Mimarlık Ofisi

Mimari Uygulama Projesi

YAPI YERİ

Tekirdağ / Süleymanpaşa

Gündoğdu Mah.

Ada 2758 · Parsel 4

Parsel alanı: 755,60 m²

İŞVEREN

PRIME OFİS MİMARLIK

MİMAR / ÇİZEN

Ad Soyad: .....

Oda Sicil No: .....

İmza: .....

TARİH

22.10.2026

PAFTA ADI

VAZİYET PLANI

ÖLÇEK


1/250 · 1/5000

PAFTA NO

01

ZEMİN KAT PLANI

Ölçek 1/50 · Kot ±0.00 = +129.60 (mutlak)

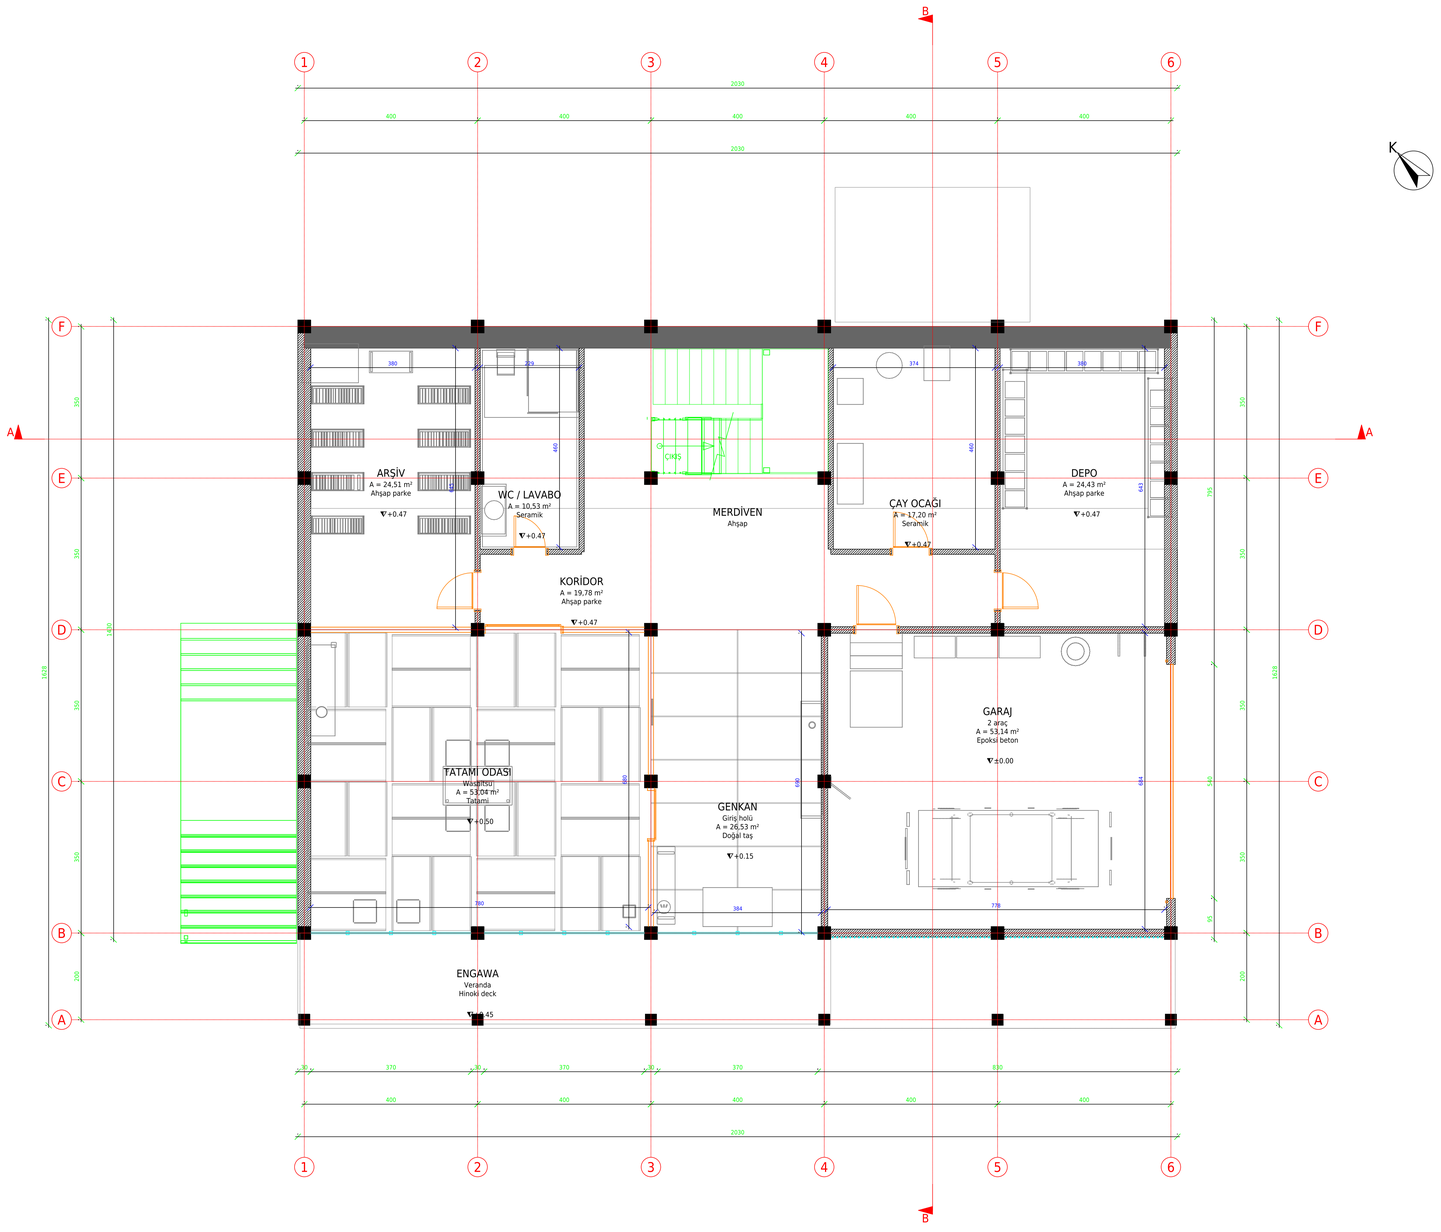

NOTLAR

Ölçüler cm, kotlar m cinsindendir. ±0.00 = +129.60 (mutlak).

Dış ölçü zincirleri: (1) açıklık/dolu, (2) aks, (3) toplam. İç ölçüler bitmiş yüzeyler arasıdır.

Taşıyıcı sistem: 30x30 cm tutkallı lamine ahşap kolon, GL24h kiriş, CLT döşeme; zemin kat kuzey duvarı betonarme istinat perdesidir.

Kesik çizgi: üstte kalan saçak / balkon / çatı izdüşümü.

Tüm ölçüler uygulama öncesi yerinde kontrol edilecektir.

LEJANT

- Duvar kesiti
- Betonarme kesit
- Ahşap kolon 30x30
- Pencere / cam
- Kapı
- Mobilya / donatı
- Üst görünüş (kesik)
- Aks
- Kesit hattı

PROJE

PRIME OFİS

3 Katlı Mimarlık Ofisi

Mimari Uygulama Projesi

YAPI YERİ

Tekirdağ / Süleymanpaşa

Gündoğdu Mah.

Ada 2758 · Parsel 4

Parsel alanı: 755,60 m²

İŞVEREN

PRIME OFİS MİMARLIK

MİMAR / ÇİZEN

Ad Soyad: .....

Oda Sicil No: .....

İmza: .....

TARİH

22.10.2026

PAFTA ADI

ZEMİN KAT PLANI

ÖLÇEK


1/50

PAFTA NO

02

1. KAT PLANI

Ölçek 1/50 · Döşeme üst kotu +3.97

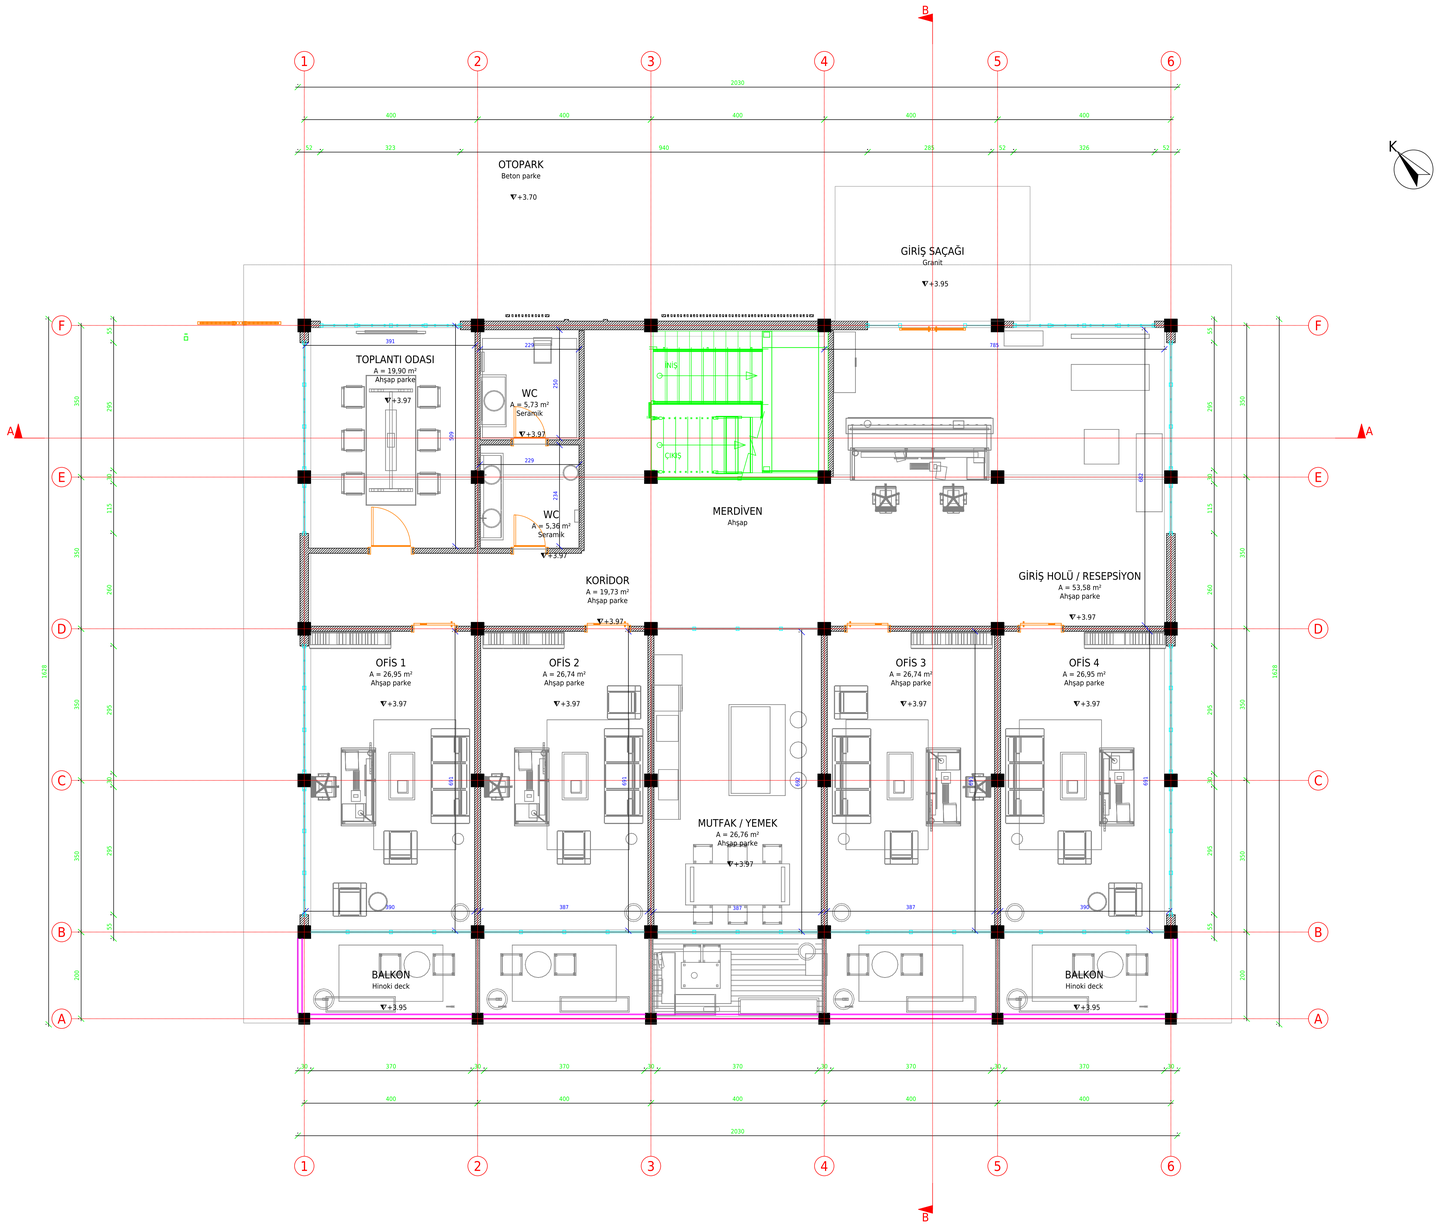

NOTLAR

Ölçüler cm, kotlar m cinsindendir. ±0.00 = +129.60 (mutlak).

Dış ölçü zincirleri: (1) açıklık/dolu, (2) aks, (3) toplam. İç ölçüler bitmiş yüzeyler arasıdır.

Taşıyıcı sistem: 30x30 cm tutkallı lamine ahşap kolon, GL24h kiriş, CLT döşeme; zemin kat kuzey duvarı betonarme istinat perdesidir.

Kesik çizgi: üstte kalan saçak / balkon / çatı izdüşümü.

Tüm ölçüler uygulama öncesi yerinde kontrol edilecektir.

LEJANT

- Duvar kesiti
- Betonarme kesit
- Ahşap kolon 30x30
- Pencere / cam
- Kapı
- Mobilya / donatı
- Üst görünüş (kesik)
- Aks
- Kesit hattı

PROJE

PRIME OFİS

3 Katlı Mimarlık Ofisi

Mimari Uygulama Projesi

YAPI YERİ

Tekirdağ / Süleymanpaşa

Gündoğdu Mah.

Ada 2758 · Parsel 4

Parsel alanı: 755,60 m²

İŞVEREN

PRIME OFİS MİMARLIK

MİMAR / ÇİZEN

Ad Soyad: .....

Oda Sicil No: .....

İmza: .....

TARİH

22.10.2026

PAFTA ADI

1. KAT PLANI

ÖLÇEK


1/50

PAFTA NO

03

2. KAT PLANI

Ölçek 1/50 · Döşeme üst kotu +7.47

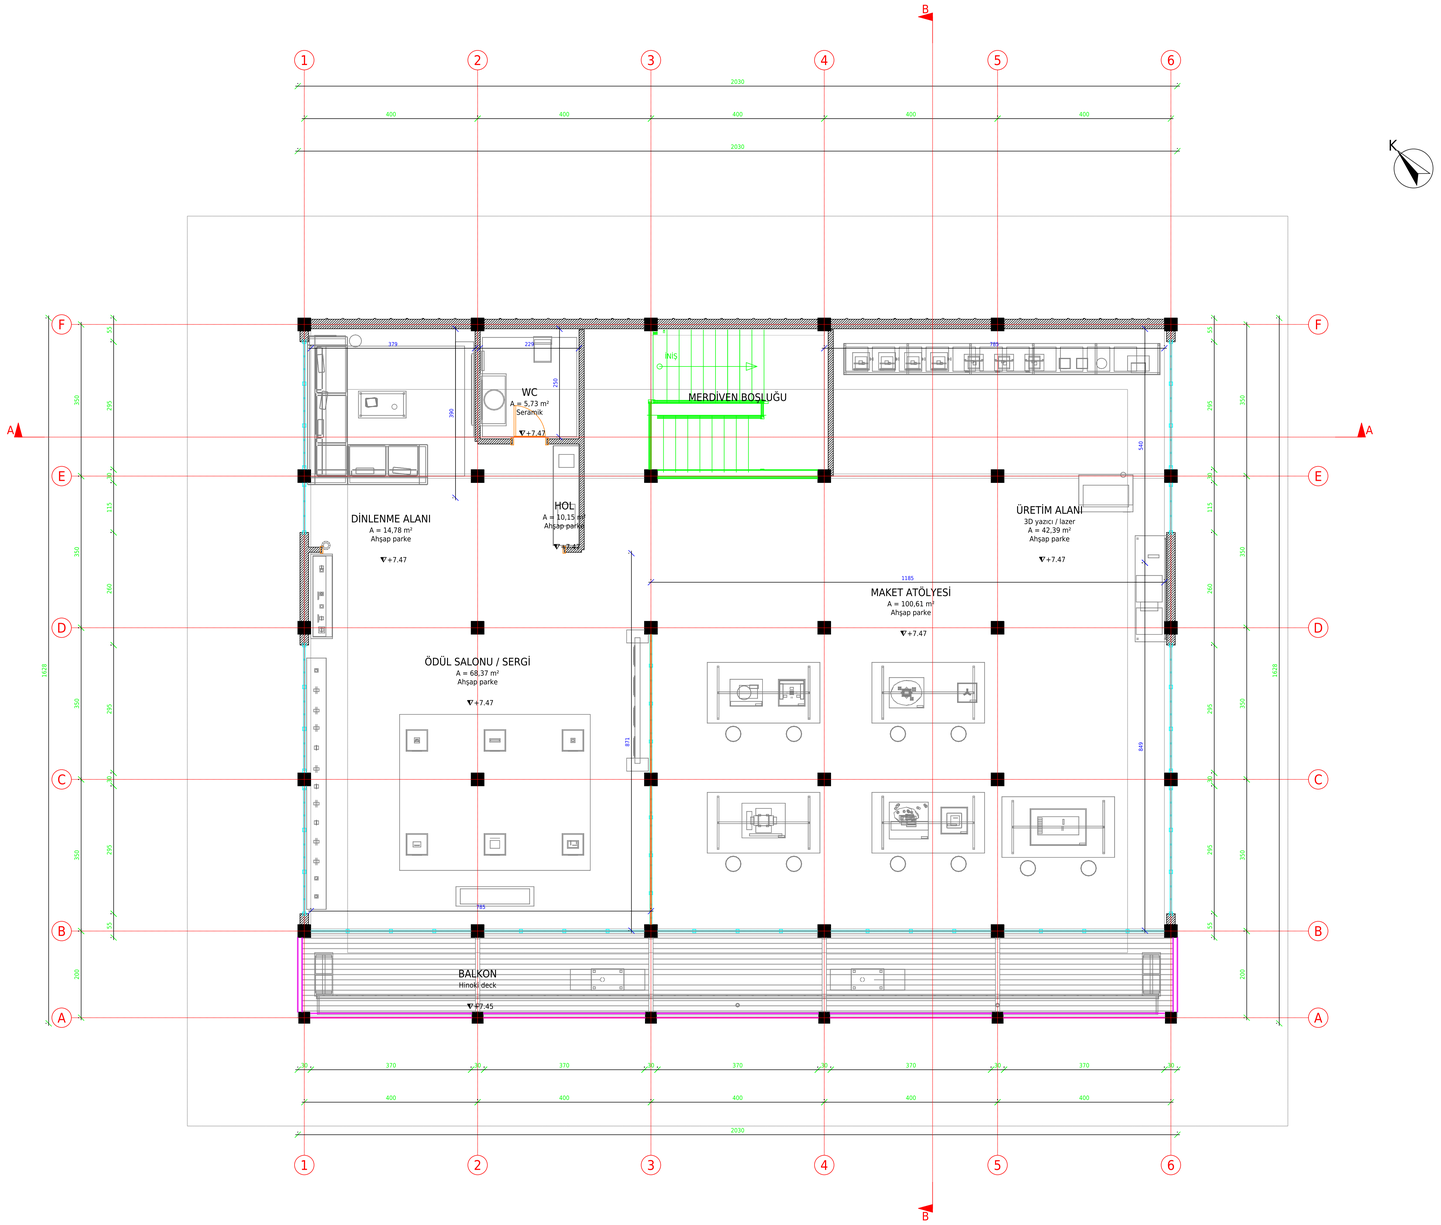

NOTLAR

Ölçüler cm, kotlar m cinsindendir. ±0.00 = +129.60 (mutlak).

Dış ölçü zincirleri: (1) açıklık/dolu, (2) aks, (3) toplam. İç ölçüler bitmiş yüzeyler arasıdır.

Taşıyıcı sistem: 30x30 cm tutkallı lamine ahşap kolon, GL24h kiriş, CLT döşeme; zemin kat kuzey duvarı betonarme istinat perdesidir.

Kesik çizgi: üstte kalan saçak / balkon / çatı izdüşümü.

Tüm ölçüler uygulama öncesi yerinde kontrol edilecektir.

LEJANT

- Duvar kesiti
- Betonarme kesit
- Ahşap kolon 30x30
- Pencere / cam
- Kapı
- Mobilya / donatı
- Üst görünüş (kesik)
- Aks
- Kesit hattı

PROJE

PRIME OFİS

3 Katlı Mimarlık Ofisi

Mimari Uygulama Projesi

YAPI YERİ

Tekirdağ / Süleymanpaşa

Gündoğdu Mah.

Ada 2758 · Parsel 4

Parsel alanı: 755,60 m²

İŞVEREN

PRIME OFİS MİMARLIK

MİMAR / ÇİZEN

Ad Soyad: .....

Oda Sicil No: .....

İmza: .....

TARİH

22.10.2026

PAFTA ADI

2. KAT PLANI

ÖLÇEK


1/50

PAFTA NO

04

KESİT A-A

Ölçek 1/50 · Merdivenden geçen kesit, kuzeye bakış

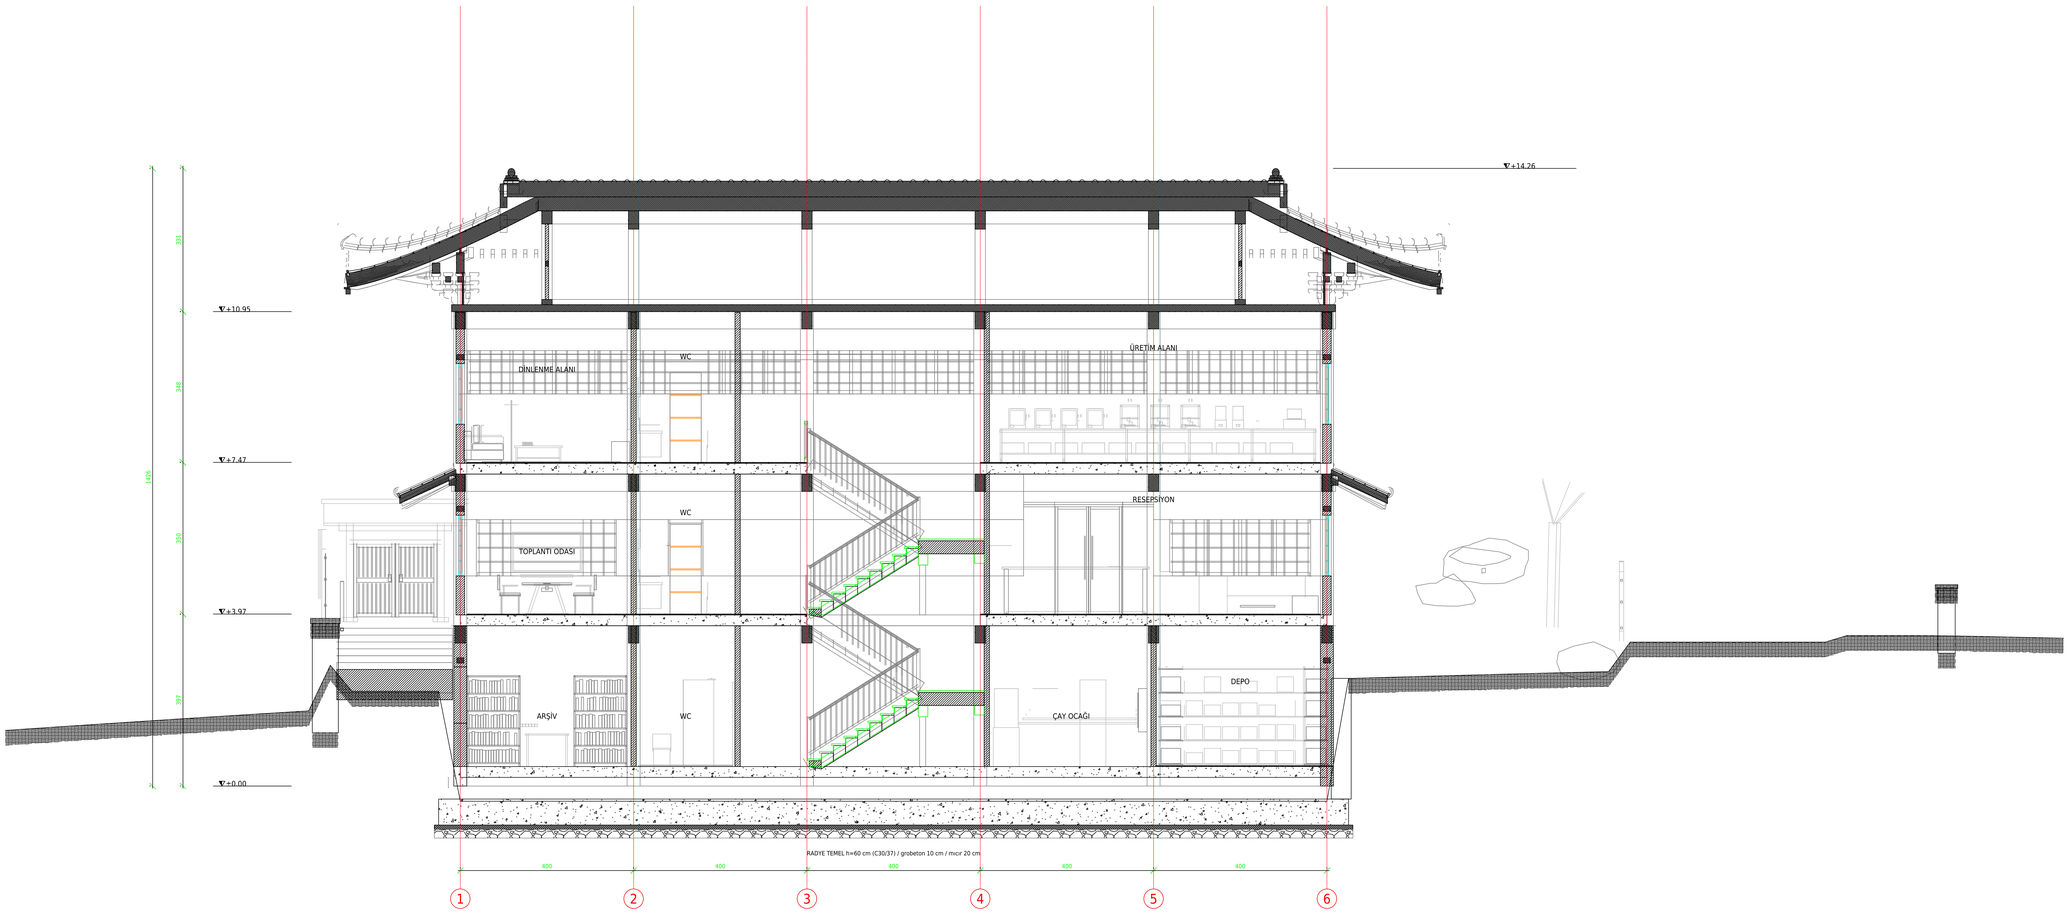

NOTLAR

Ölçüler cm, kotlar m cinsindendir. ±0.00 = +129.60.

Kalın çizgi: kesilen elemanlar; ince/gri çizgi: görünüşte kalan elemanlar.

Temel sistemi: radye temel (bkz. D1). Döşemeler: CLT 18 cm (bkz. D2).

Çatı: kiremit (hongawara) kaplı ahşap kırma çatı, kumimono konsol sistemi.

LEJANT

- Betonarme
- Ahşap (kesit)
- Duvar
- Toprak
- Zemin kesit hattı
- Görünüş

PROJE

PRIME OFİS

3 Katlı Mimarlık Ofisi

Mimari Uygulama Projesi

YAPI YERİ

Tekirdağ / Süleymanpaşa

Gündoğdu Mah.

Ada 2758 · Parsel 4

Parsel alanı: 755,60 m²

İŞVEREN

PRIME OFİS MİMARLIK

MİMAR / ÇİZEN

Ad Soyad: .....

Oda Sicil No: .....

İmza: .....

TARİH

22.10.2026

PAFTA ADI

KESİT A-A

ÖLÇEK


1/50

PAFTA NO

05

KESİT B-B

Ölçek 1/50 · Garaj, ofis ve girişten geçen kesit, batıya bakış

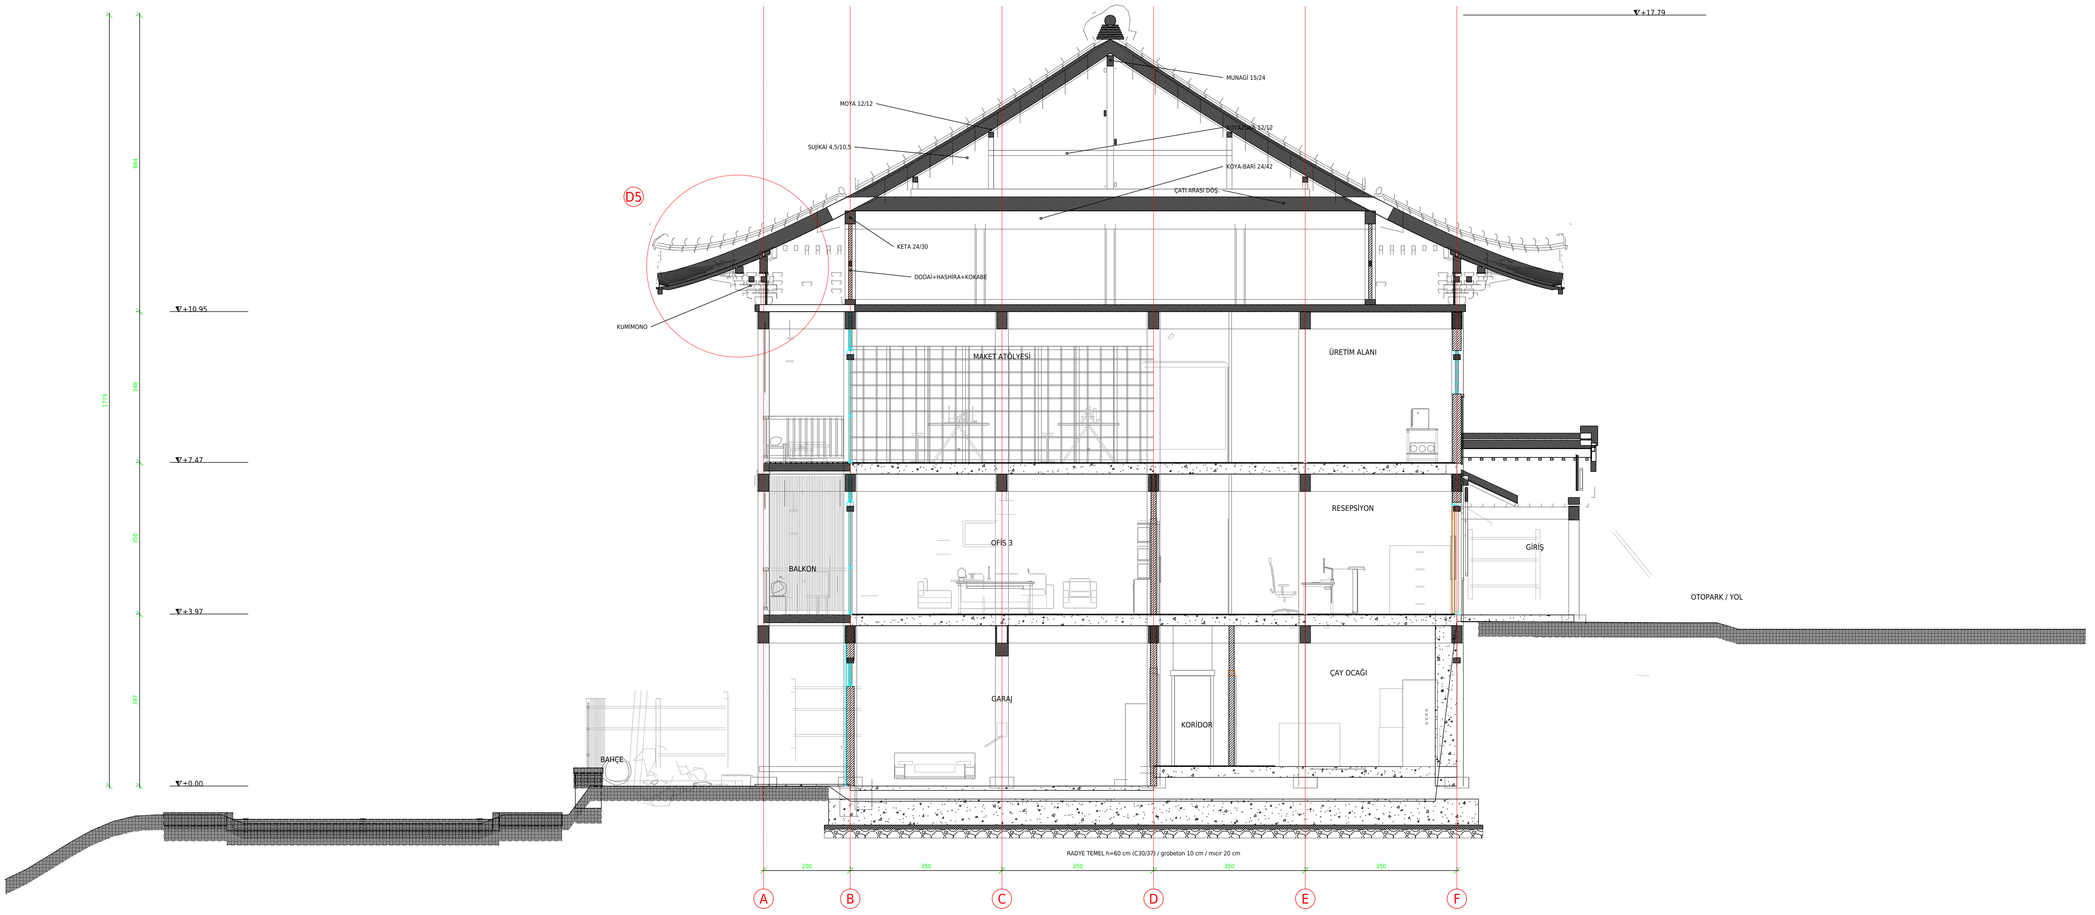

NOTLAR

Ölçüler cm, kotlar m cinsindendir. ±0.00 = +129.60.

Kalın çizgi: kesilen elemanlar; ince/gri çizgi: görünüşte kalan elemanlar.

Temel sistemi: radye temel (bkz. D1). Döşemeler: CLT 18 cm (bkz. D2).

Çatı: kiremit (hongawara) kaplı ahşap kırma çatı, kumimono konsol sistemi.

LEJANT

- Betonarme
- Ahşap (kesit)
- Duvar
- Toprak
- Zemin kesit hattı
- Görünüş

PROJE

PRIME OFİS

3 Katlı Mimarlık Ofisi

Mimari Uygulama Projesi

YAPI YERİ

Tekirdağ / Süleymanpaşa

Gündoğdu Mah.

Ada 2758 · Parsel 4

Parsel alanı: 755,60 m²

İŞVEREN

PRIME OFİS MİMARLIK

MİMAR / ÇİZEN

Ad Soyad: .....

Oda Sicil No: .....

İmza: .....

TARİH

22.10.2026

PAFTA ADI

KESİT B-B


ÖLÇEK

1/50

PAFTA NO


06

D1 TEMEL VE ZEMİN DÖŞEMESİ DETAYI 1/10

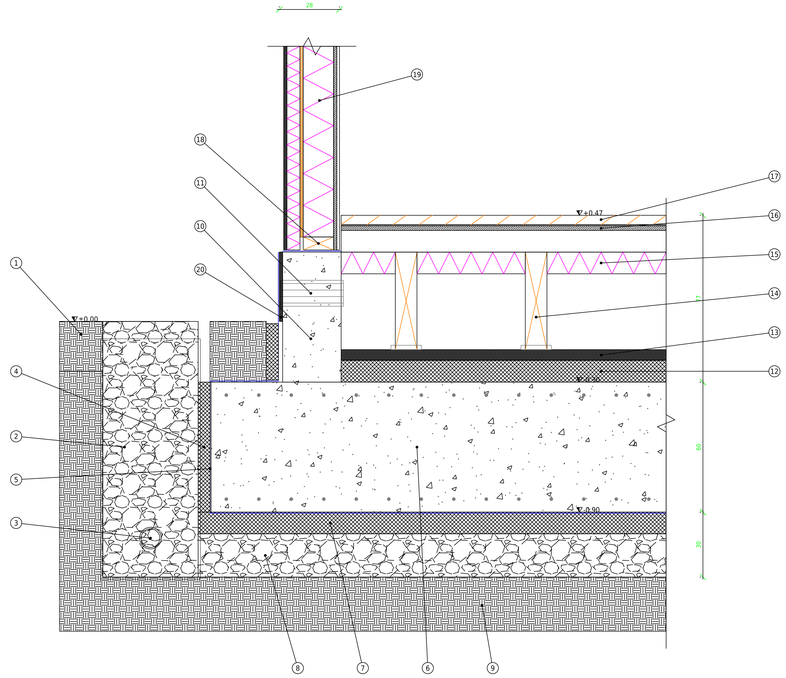

1. Bitkisel toprak / çakıl şerit (yağmur sıçrama koruması)
2. Drenaj çakılı 16-32 mm, geotekstil sargılı
3. Delikli drenaj borusu Ø100 (%1 eğimli, rögara bağlı)
4. Perimetre ısı yalıtımı XPS 6 cm
5. Bitümlü membran su yalıtımı 2 kat (4+4 mm) + koruma levhası
6. Radye temel h=60 cm, C30/37 / B500C, çift sıra donatı
7. Grobeton 10 cm (C16/20)
8. Sıkıştırılmış mıcır 20 cm
9. Sıkıştırılmış doğal zemin
10. Betonarme subasman perdesi 27 cm
11. Döşeme altı havalandırma menfezi, paslanmaz ızgara (her 2 m'de)
12. Döşeme altı ısı yalıtımı XPS 10 cm + PE folyo
13. Tesviye şapı 5 cm
14. Ahşap kadron 10/10 + ayarlı çelik ayak (yükseltilmiş ahşap döşeme)
15. Mineral yün 10 cm
16. OSB/3 22 mm
17. Ahşap parke 15 mm + şilte (döşeme üst kotu +0.47)
18. Taban kirişi 6/14 + bitümlü yatay su yalıtım bandı
19. Ahşap karkas dış duvar (bkz. D2)
20. Su itici subasman sıvası


D2 DIŞ DUVAR – ARA KAT DÖŞEMESİ DETAYI 1/10

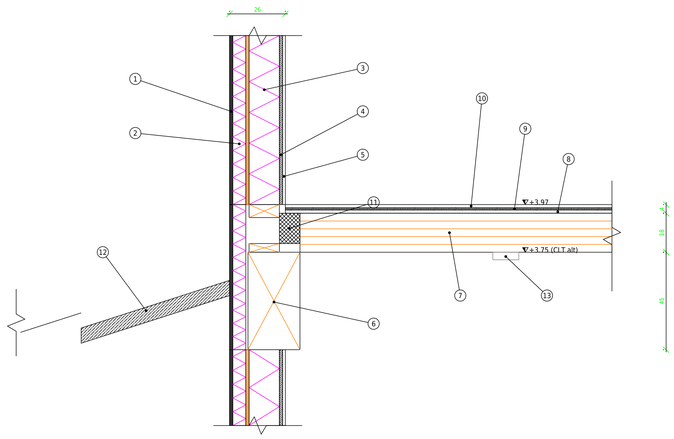

1. Dış cephe sıvası 15 mm, silikat esaslı, file takviyeli
2. Odun lifi yalıtım levhası 60 mm (sıva taşıyıcı)
3. Ahşap dikme 6/14 @62,5 cm + odun lifi şilte 140 mm
4. OSB/3 15 mm (buhar kesici bantlı)
5. Alçı levha 12,5 mm, boyalı
6. Tutkallı lamine kiriş GL24h 24/45
7. Çapraz lamine ahşap döşeme (CLT) 180 mm, alt yüzey açık ladin
8. Darbe sesi yalıtım şiltesi 15 mm
9. Kuru şap levhası 10 mm
10. Ahşap parke 15 mm (üst kot +3.97)
11. Isı yalıtımı (kiriş başı) mineral yün
12. Saçak (mokoshi) dikmesi / konsol, hinoki
13. Gömme LED aydınlatma profili

D3 PENCERE DETAYI 1/5


DÜŞEY KESİT: DENİZLİK (alt) / LENTO (üst)

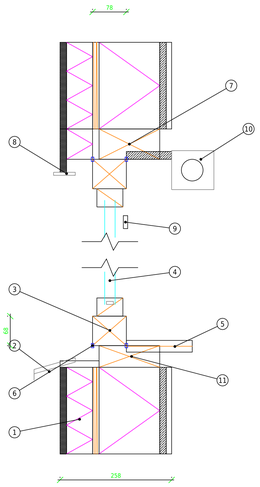


1. Dış duvar (bkz. D2)
2. Alüminyum denizlik, damlalıklı, %5 eğimli
3. Ahşap pencere kasası 68/78 (meşe, yağ emprenye)
4. Ahşap kanat + 4/16/4 Low-E çift cam, sıcak kenar ara çıta
5. İç denizlik, hinoki 30 mm
6. Dış: difüzyon açık / iç: buhar kesici bant (çevre)
7. Ahşap lento 14/7
8. Damlalık profili
9. Kumiko ahşap kafes çıtası
10. Stor perde kutusu (washi kâğıt stor)
11. Taban kirişi / denizlik altı kadronu

D4 KAPI DETAYLARI 1/5

(a) SÜRME OFİS KAPISI – DÜŞEY KESİT

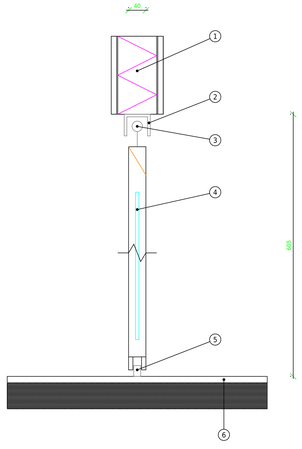

(b) MENTEŞELİ KAPI KASASI – YATAY KESİT

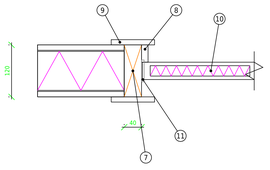

1. Bölme duvar: ahşap dikme 5/9 + mineral yün, 2×12,5 mm alçı levha
2. Alüminyum üst ray, gizli, tavana gömme
3. Bilyalı makara + askı, yumuşak kapanma
4. Sürme kapı kanadı 40 mm, ahşap çerçeve + buzlu cam 8 mm
5. Zemin kılavuz pimi (paslanmaz)
6. Ahşap parke 15 mm / şap
7. Ahşap kasa 40/120, hinoki
8. Kapı stoperi + fitil
9. Pervaz 10/70
10. Kapı kanadı 40 mm, ahşap çerçeve + yalıtım dolgu
11. Gizli menteşe (3 adet)

NOTLAR

D1/D2 ölçüleri cm, D3/D4 ölçüleri mm cinsindendir.

Ahşap elemanlar: GL24h / C24, koruyucu emprenyeli; dış yüzeyde yakısugi (kömürleştirilmiş sedir) uygulanan yerler cephe planında gösterilmiştir.

Su yalıtımı TS EN 13707'ye uygun bitümlü membran; tüm bindirmeler en az 10 cm.

Detaylar sistem detayı niteliğindedir; uygulama detayları statik proje ile birlikte kesinleştirilecektir.

LEJANT

- Beton / betonarme
- Sert ısı yalıtımı (XPS)
- Çakıl / mıcır
- Toprak
- Su yalıtımı (membran)
- Yumuşak yalıtım (zikzak)

PROJE

PRIME OFİS

3 Katlı Mimarlık Ofisi

Mimari Uygulama Projesi

YAPI YERİ

Tekirdağ / Süleymanpaşa

Gündoğdu Mah.

Ada 2758 · Parsel 4

Parsel alanı: 755,60 m²

İŞVEREN

PRIME OFİS MİMARLIK

MİMAR / ÇİZEN

Ad Soyad: .....

Oda Sicil No: .....

İmza: .....

TARİH

22.10.2026

PAFTA ADI

SİSTEM DETAYLARI


ÖLÇEK

1/10 · 1/5

PAFTA NO


07

D5 ÇATI – DUVAR (SAÇAK) BİRLEŞİM DETAYI 1/20

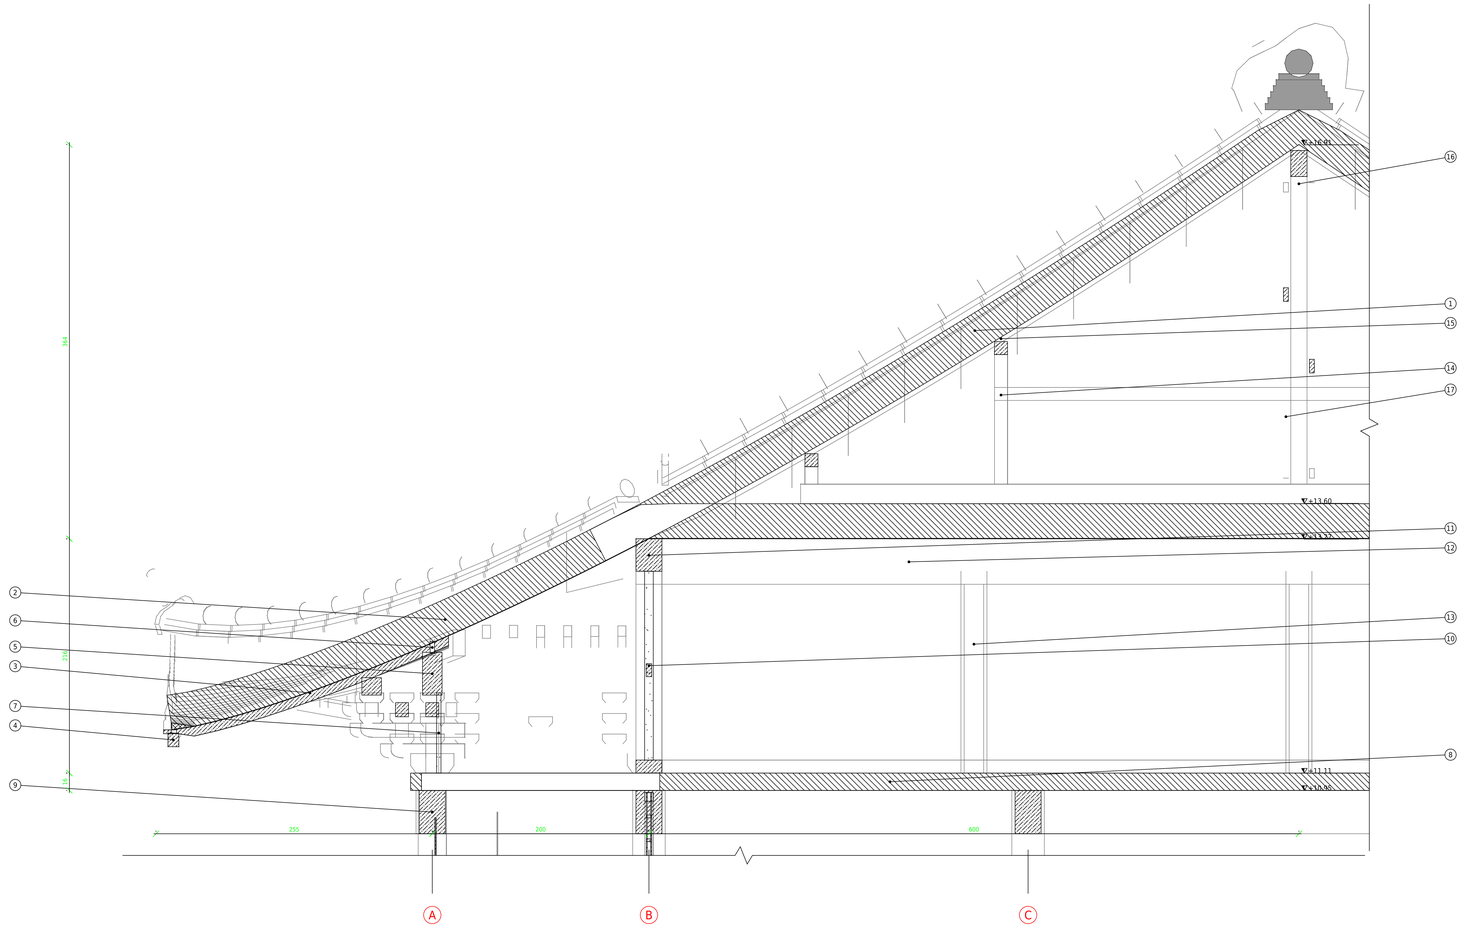

1. Üst çatı katmanları: 24 mm ahşap kaplama (nojiita) + 2 kat bitümlü altlık membran + çıta; tarıaki 6/9 @45 cm
2. Etek (mokoshi) çatısı ve çatı arası döşemesi: ahşap kaplama + altlık membranı; iç kısımda 32 cm kaplamalı yatay döşeme
3. Taruki – saçak mertekleri 6/9 cm @30 cm, ji-daruki + hi-daruki (çift sıra)
4. Kayaoi / urako – saçak ucu alın kirişi ve mertek ucu kapama tahtası (bakır kenar)
5. Gangyo-keta – saçak taşıyıcı aşığı 18/30 cm, konsollar üzerine oturur
6. Menko-ita – konsol aralarını kapatan tahta
7. Kokabe – konsol araları kireç sıva dolgu, ahşap çerçeve içinde
8. Çatı katı döşemesi: CLT 16 cm, üstünde buhar dengeleyici + 10 cm taş yünü + OSB yürüme yüzeyi
9. Hari / ana kiriş – GL24h, döşemeyi taşır
10. Çatı arası duvarı: dodai 24/12 + hashira 24/24 + nuki 4/12, arası komai üzeri kireç sıva 8 cm
11. Keta – üst çatı ve etek çatısını taşıyan başlık aşığı 24/30 (çevre çerçevesi)
12. Koya-bari – çatı arası tavanı/döşeme kirişi 24/42 GL24h, 4 m aralıklı aks hatlarında
13. Tsuka – hari altı ara dikme 18/18 (y = -4,0 / -1,0 / +2,0 aks hatları)
14. Koyazuka – çatı dikmeleri 12/12, koyabari (15/18) üzerine oturur; nuki 3/12 ile bağlı
15. Moya – aşık 12/12, ~1,75 m aralıklı
16. Munagi – mahya kirişi 15/24, munezuka dikmeleri 15/15 üzerinde
17. Koya-sujikai – mahya doğrultusunda çapraz bağ 4,5/10,5

D6 ÇATI KONSTRÜKSİYON PLANI (+13,27) 1/100

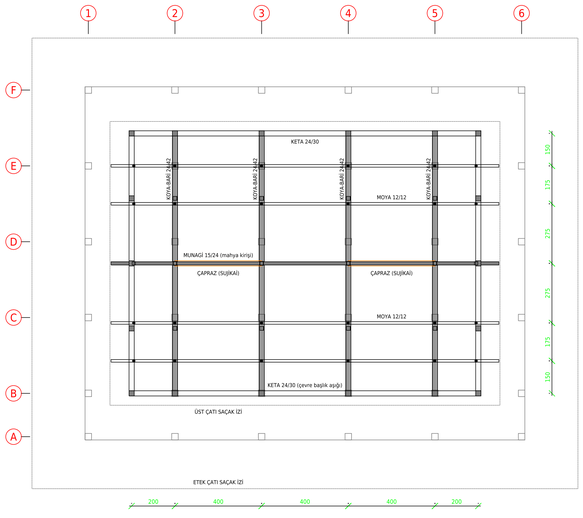

NOTLAR

D5, Kesit B-B (aks 4-5 arası, x = +4,50) hattından alınmıştır; ölçüler cm, kotlar m cinsindendir.

Çatı sistemi geleneksel wagoya (Japon çatı iskeleti) mantığındadır: çevre keta çerçevesi + koya-bari + koyazuka + moya + munagi.

Saçak yükü kumimono konsol sistemi (daito-masu-hijiki) üzerinden kolon başlarına aktarılır; konsol araları kokabe ile kapatılır.

Tüm taşıyıcı ahşaplar GL24h / C24, emprenyeli. Birleşimler geleneksel geçme (ari / kama) + gizli çelik bulon ile yapılacaktır.

Çatı arası havalandırması mahya ve saçak altı (noki-ura) havalandırma boşlukları ile sağlanır; yalıtım tavan döşemesi üzerindedir.

Kesin eleman boyutları statik hesaba göre belirlenecektir.

LEJANT

- Kesilen eleman
- Görünüşte kalan eleman
- Ahşap (kesit)
- Kireç sıva dolgu
- Saçak izdüşümü

PROJE

PRIME OFİS

3 Katlı Mimarlık Ofisi

Mimari Uygulama Projesi

YAPI YERİ

Tekirdağ / Süleymanpaşa

Gündoğdu Mah.

Ada 2758 · Parsel 4

Parsel alanı: 755,60 m²

İŞVEREN

PRIME OFİS MİMARLIK

MİMAR / ÇİZEN

Ad Soyad: .....

Oda Sicil No: .....

İmza: .....

TARİH

22.10.2026

PAFTA ADI

ÇATI DETAYLARI

ÖLÇEK

1/20 · 1/100

PAFTA NO

08